


NORD-LOCK

26 ST KONTORSPLATSER
CA 396 KVM (OBS! YTA MÄTT
PÅ ÄLDRE
RITNINGСУNDERLAG - EJ
KONTROLLERAT PÅ PLATS

PLAN 2

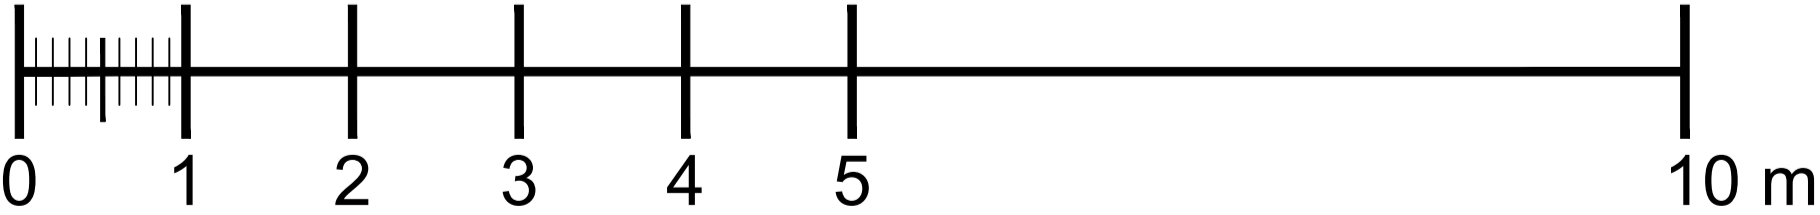

Generell information

- Aluminiummått är styrande / börjar en måttkedja.
- (5-25) = justermån 5 till 25mm på startbrädan.

Dörrmiljö

- När portal löper förbi vägg är det räknat med 30mm förbi.
- (Takutlägg livar med mötande vägg)

Aluminium: (Vid osäkerhet, dubbelkalla glasuppställning och profilval)

- Stängt aluminium används i tak
- Öppet aluminium används i golv
- Öppet aluminium mot vägg används endast vid 1st glas
- Öppet aluminium i tak används endast vid 1st glas mellan 2st portaler

Avikelser / information specificeras på planritning:

KOM IHÅG:
| Avsugning | Egenkontroll | Boka hämtning av glasstativ |

Roommejts - ritningsbeskrivning

PIDG = Portal glasad dörr 43dB

DEKO FG = DEKO FG 16,76mm Rw 42dB

Projektspecific information

- Kulör dörrmiljö = NCS S 9000-N
- Kulör profiler = RAL9005 Granular